


PROYECTO :

REMODELACIÓN ARQUITECTÓNICA
CASA CALIFORNIA

MAYO 2024

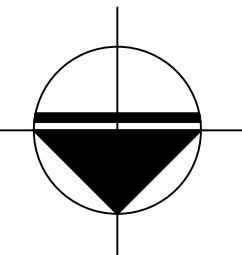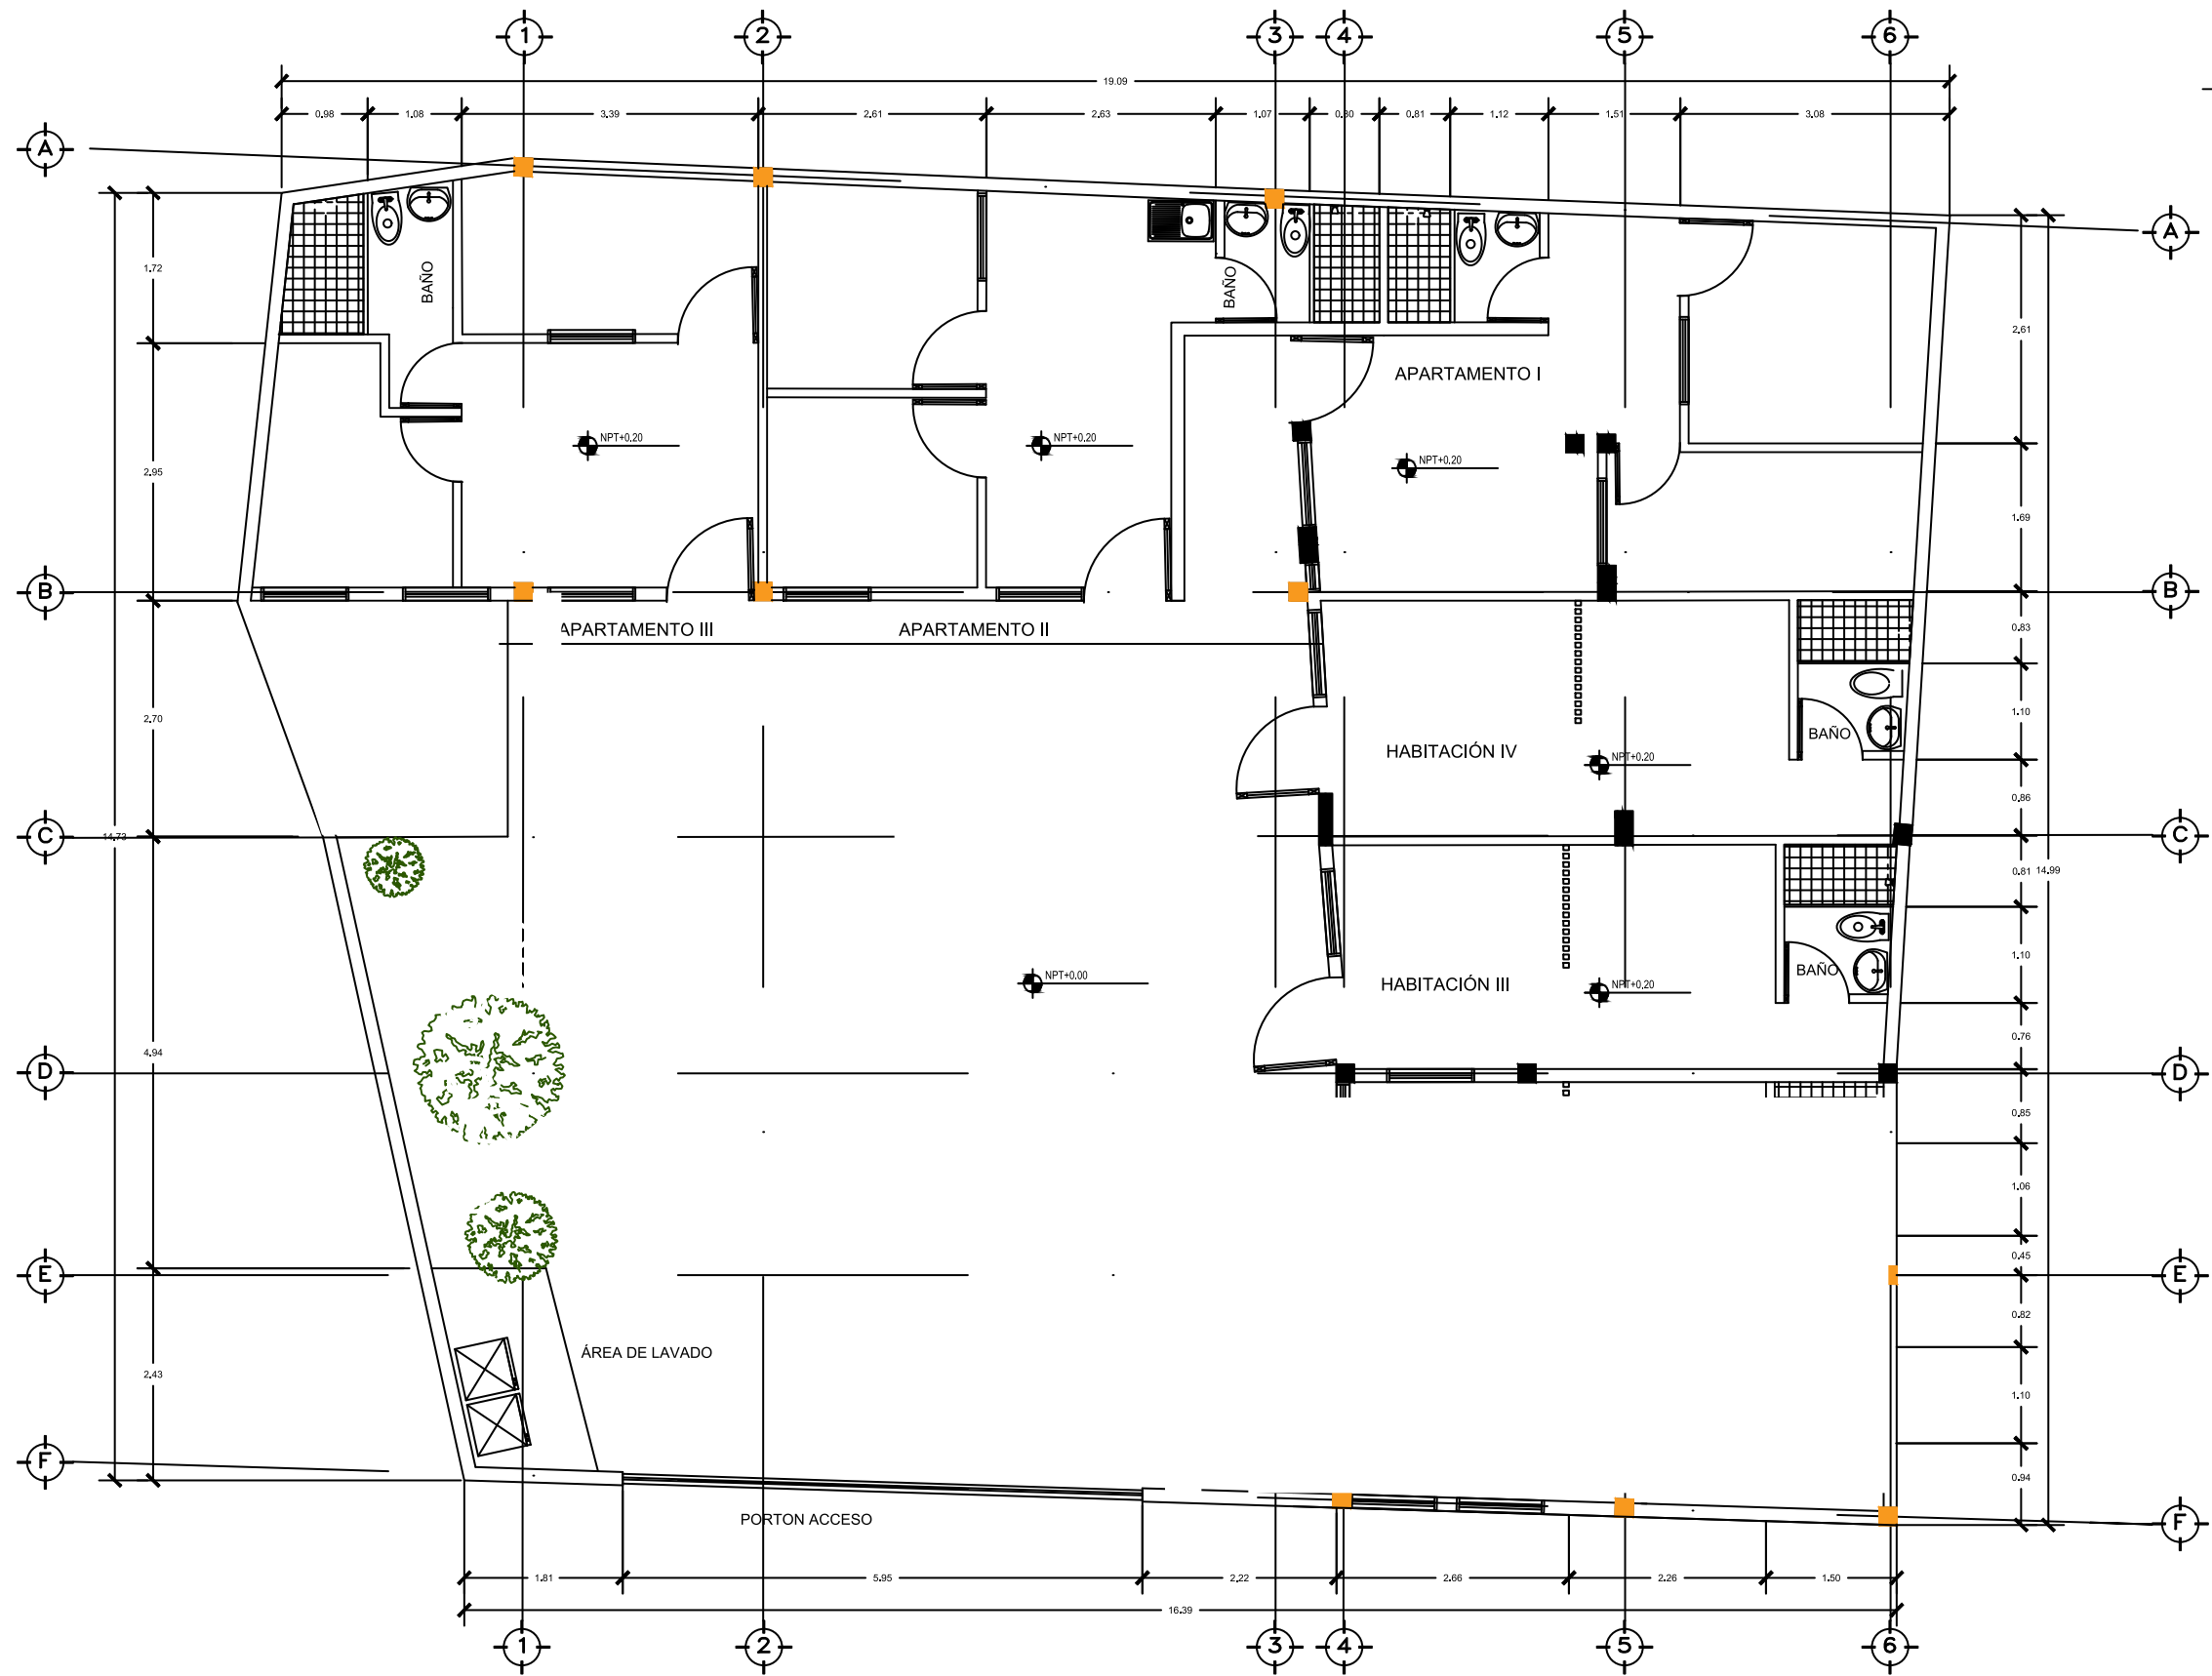

PROYECTO:

REMDELACION CASA CALIFORNIA

CONTENIDO:

PLANO ARQUITECTONICO NIVEL 1

PROYECTÓ:

ARQ. EYLEEN HERNANDEZ

ESCALA:

1:2500

FECHA:


18/05/2024

HOJA:

A1/4

PLANTA ARQUITECTÓNICA NIVEL 1



ESCALA 1:2500

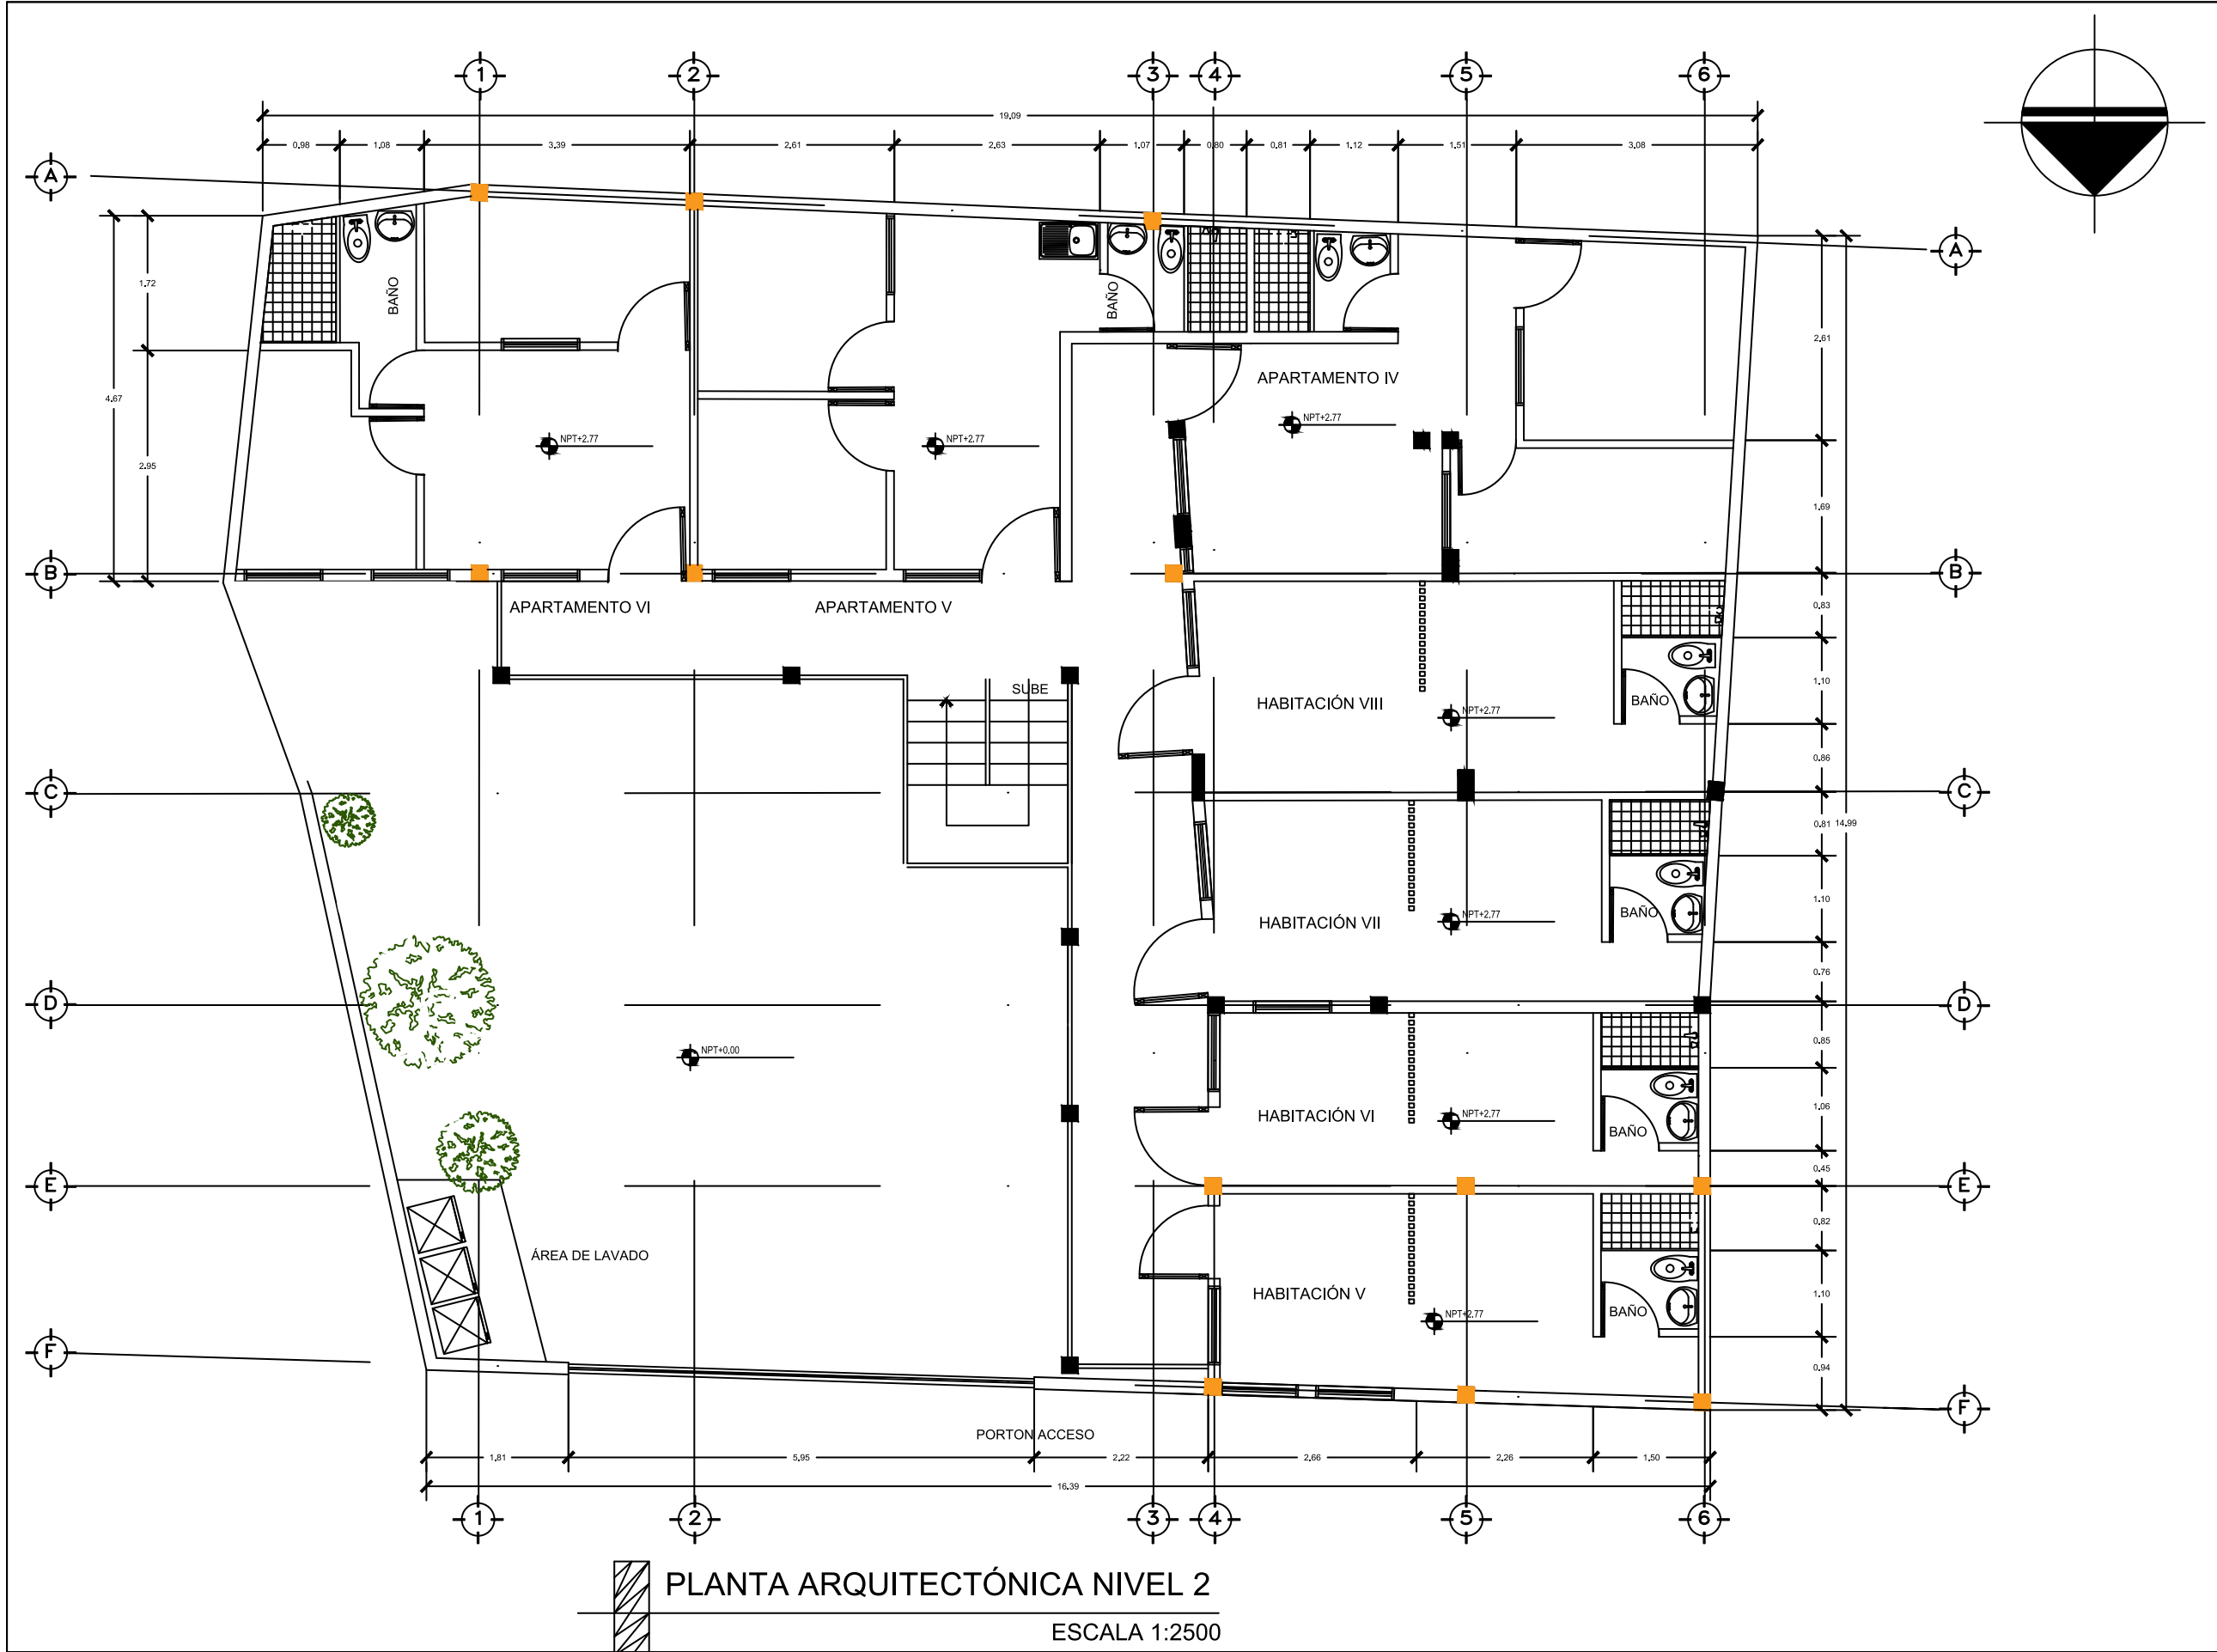

PROYECTO:	REMDELACION CASA CALIFORNIA
CONTENIDO:	PLANO ARQUITECTONICO NIVEL 2
PROYECTÓ:	ARQ. EYLEEN HERNANDEZ
ESCALA:	1:2500
FECHA:	18/05/2024
HOJA:	A2/4

PLANTA ARQUITECTÓNICA NIVEL 2

ESCALA 1:2500

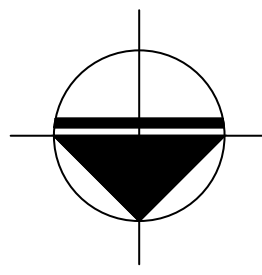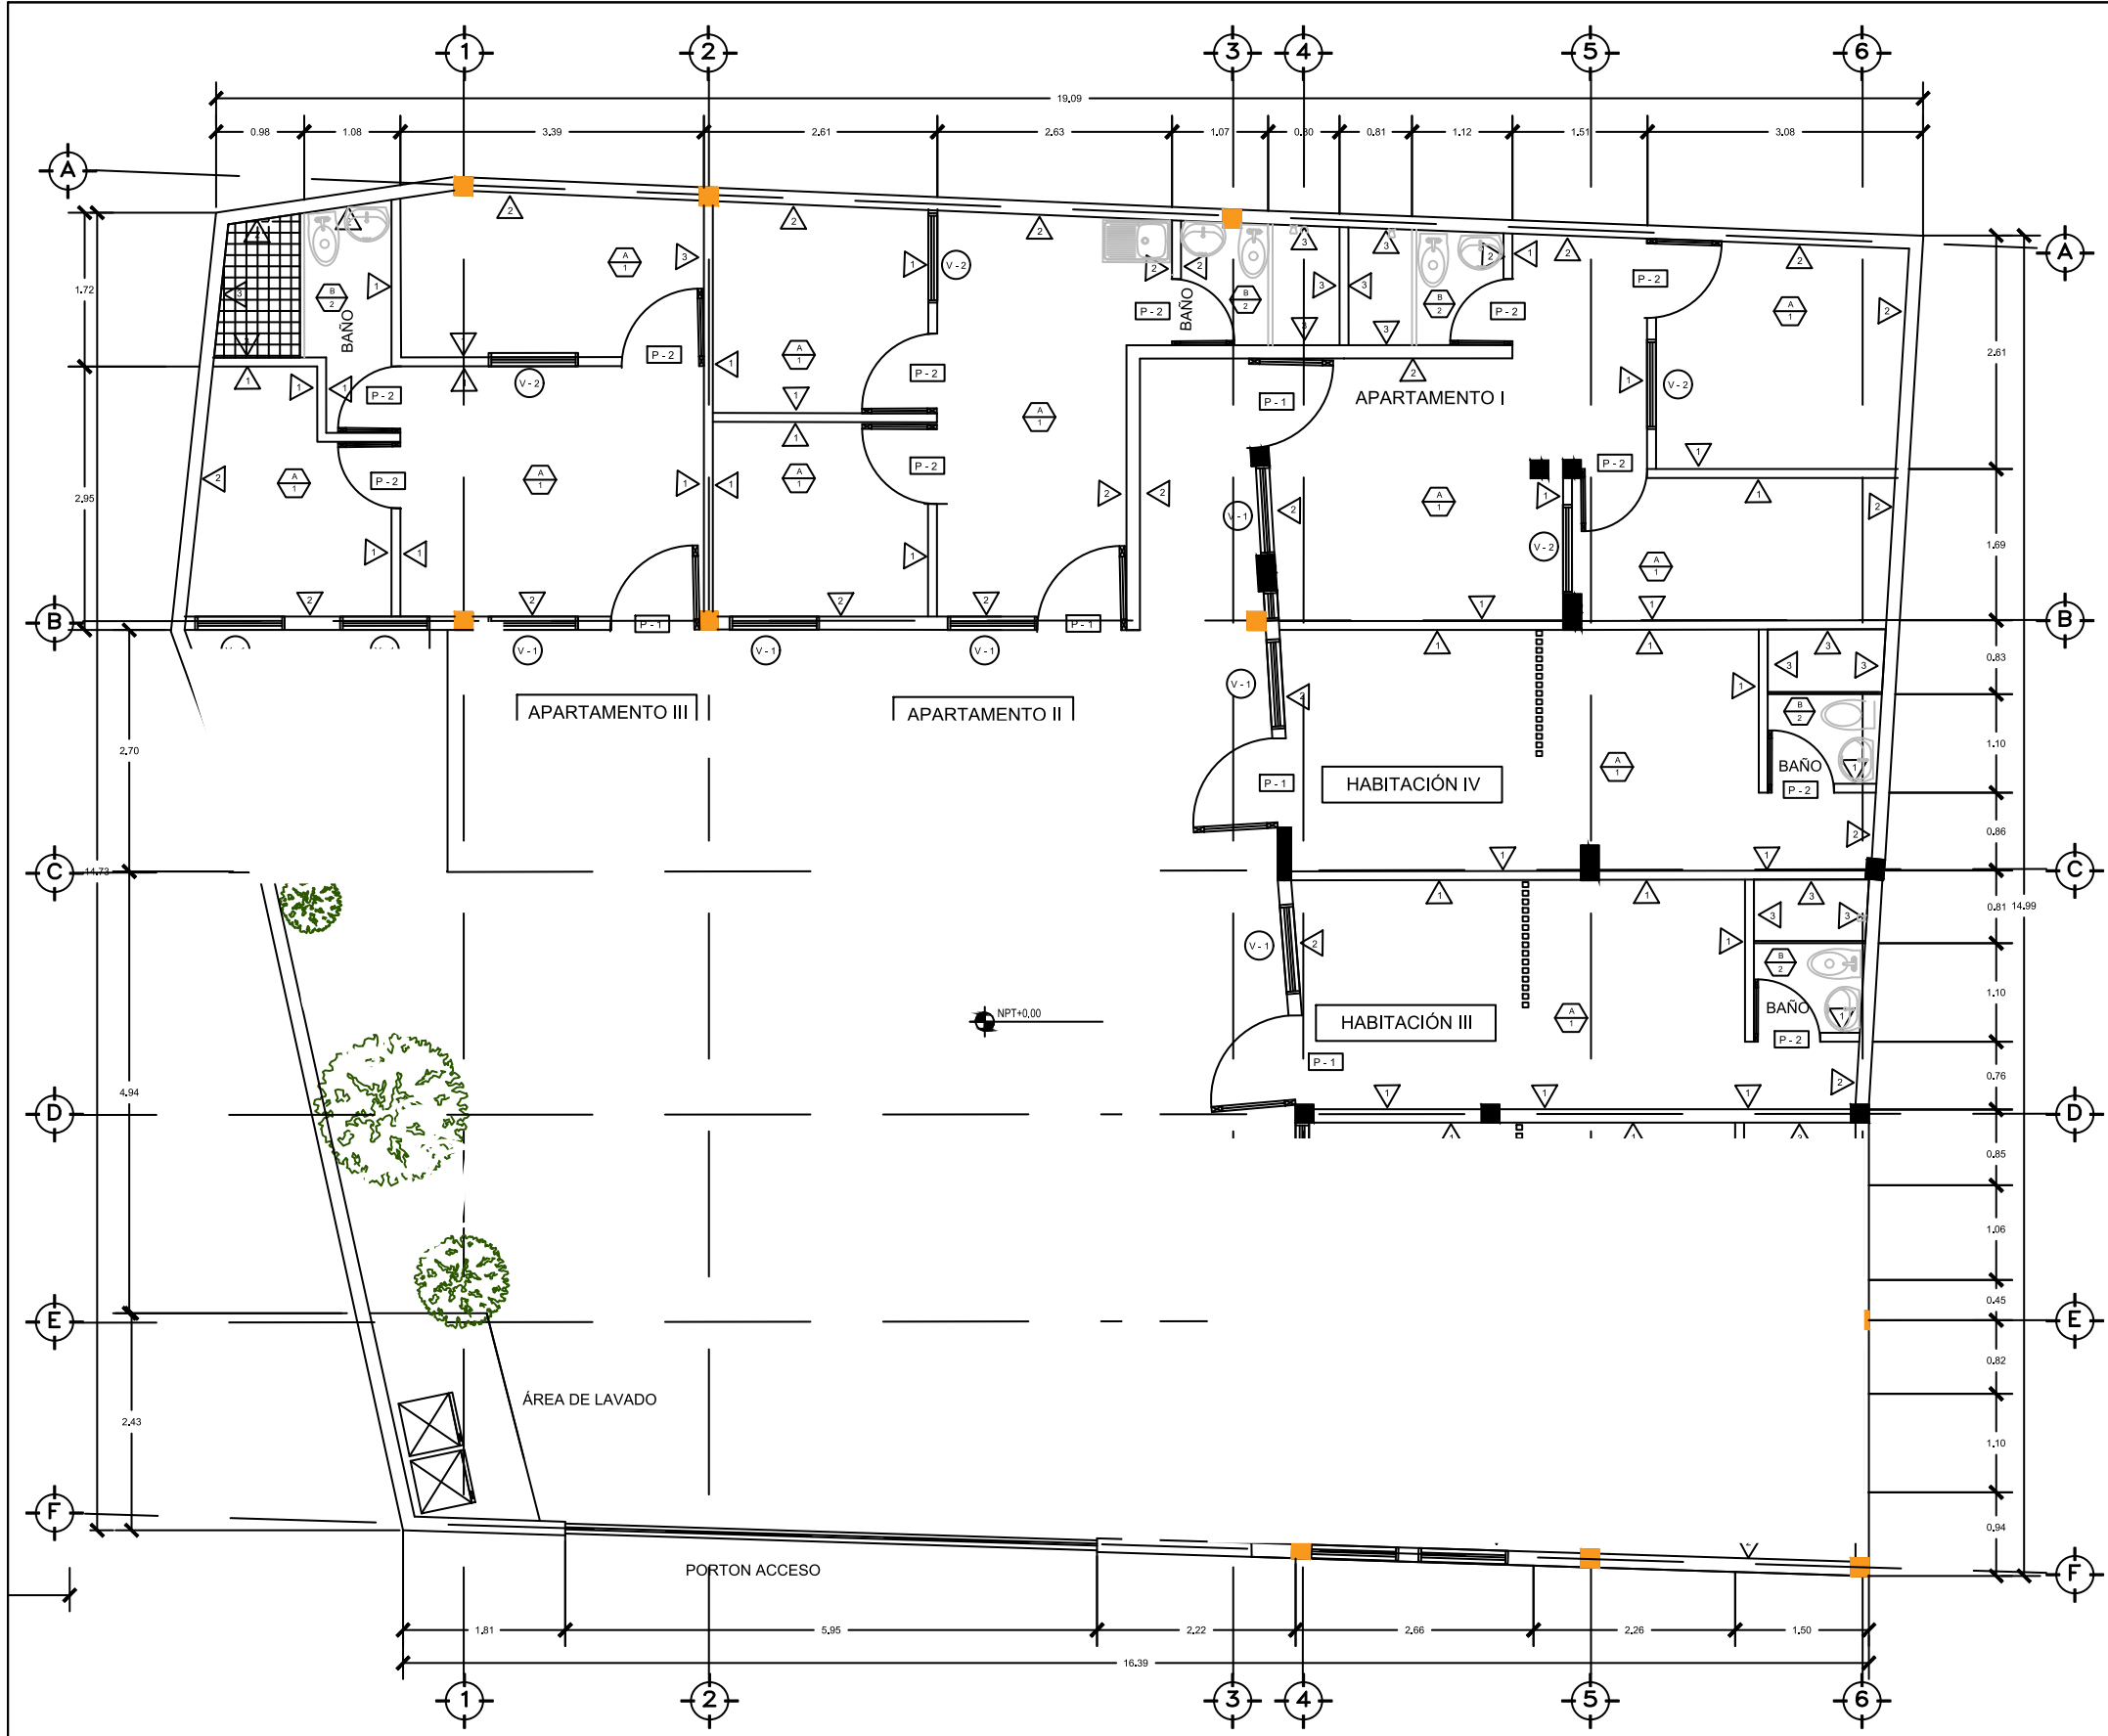

CUADRO DE PAREDES	
CLAVE	ESPECIFICACIONES TÉCNICAS
P-1	PARED DE TABLA YESO, AFINADA, LIJADA Y PINTADA, COLOR GRIS SHERWIN WILLIAMS 7064
P-2	PARED DE BLOQUE DE CONCRETO 20x40, REPELLADO, AFINADO PINTADO COLOR GRIS SHERWIN WILLIAMS 7066
P-3	PARED DE TABLAYESO, AFINADA LIJADA Y PINTADA, CON BASE ACEITE COLOR BLANCO EXCELO LATEX DENSIGLASS CON ENCHAPE DESDE NPT HASTA 1.80 MTS, PIEZA DE CERAMICO BEIGE 20X30

CUADRO DE PUERTAS			
CLAVE	ANCHO	ALTO	DESCRIPCION
P-1	1.00	2.00	PUERTA METALICA GALVANIZADA, PINTADO CON ESMALTE COLOR NEGRO.
P-2	0.74	2.00	PUERTA DE MADERA SECA, 80x110 TABLEROS, PINTADO COLOR BLANCO CON AFINADO FINAL DE BARNIZ MARINO BRILLANTE.

CUADRO DE VENTANAS			
CLAVE	ANCHO	ALTO	DESCRIPCION
V-1	1.00	1.80	VENTANAS PAREDES PERIMETRALES, VENTANAS ESTILO FRANCESA, ANTIRREFLEJO EXTERIOR MARCO DE ALUMINIO 6mm
V-2	1.00	1.20	VENTANAS PAREDES HABITACIONES, VENTANAS ESTILO FRANCESA, ANTIRREFLEJO EXTERIOR MARCO DE ALUMINIO 6mm VENTANAS ESTILO FRANCESA

CUADRO DE CIELOS	
CLAVE	ESPECIFICACIONES TÉCNICAS
C-1	CIELO FALSO DE TABLAROCA AFINADO, LIJADO PINTADO COLOR BLANCO
C-2	CIELO FALSO DE TABLAROCA DENSIGLASS AFINADO, LIJADO PINTADO COLOR BLANCO

CUADRO DE PISOS	
CLAVE	ESPECIFICACIONES TÉCNICAS
P-1	PISO CERAMICO 30X30, COLOR BEIGE EN TODAS LAS HABITACIONES
P-2	PISO CERAMICO 20x20cm antideslizante color blanco

PROYECTO:

REMODELACION CASA CALIFORNIA

CONTENIDO:

PLANO DE ACABADOS NIVEL 1

PROYECTÓ:

ARQ. EYLEEN HERNANDEZ

ESCALA:

1:2500



FECHA:

18/05/2024

HOJA:

A3/4

PLANTA ARQUITECTÓNICA NIVEL 1
ACABADOS
ESCALA 1:2500

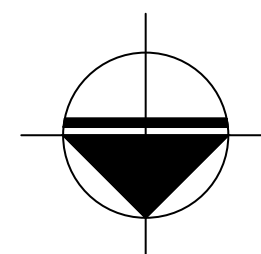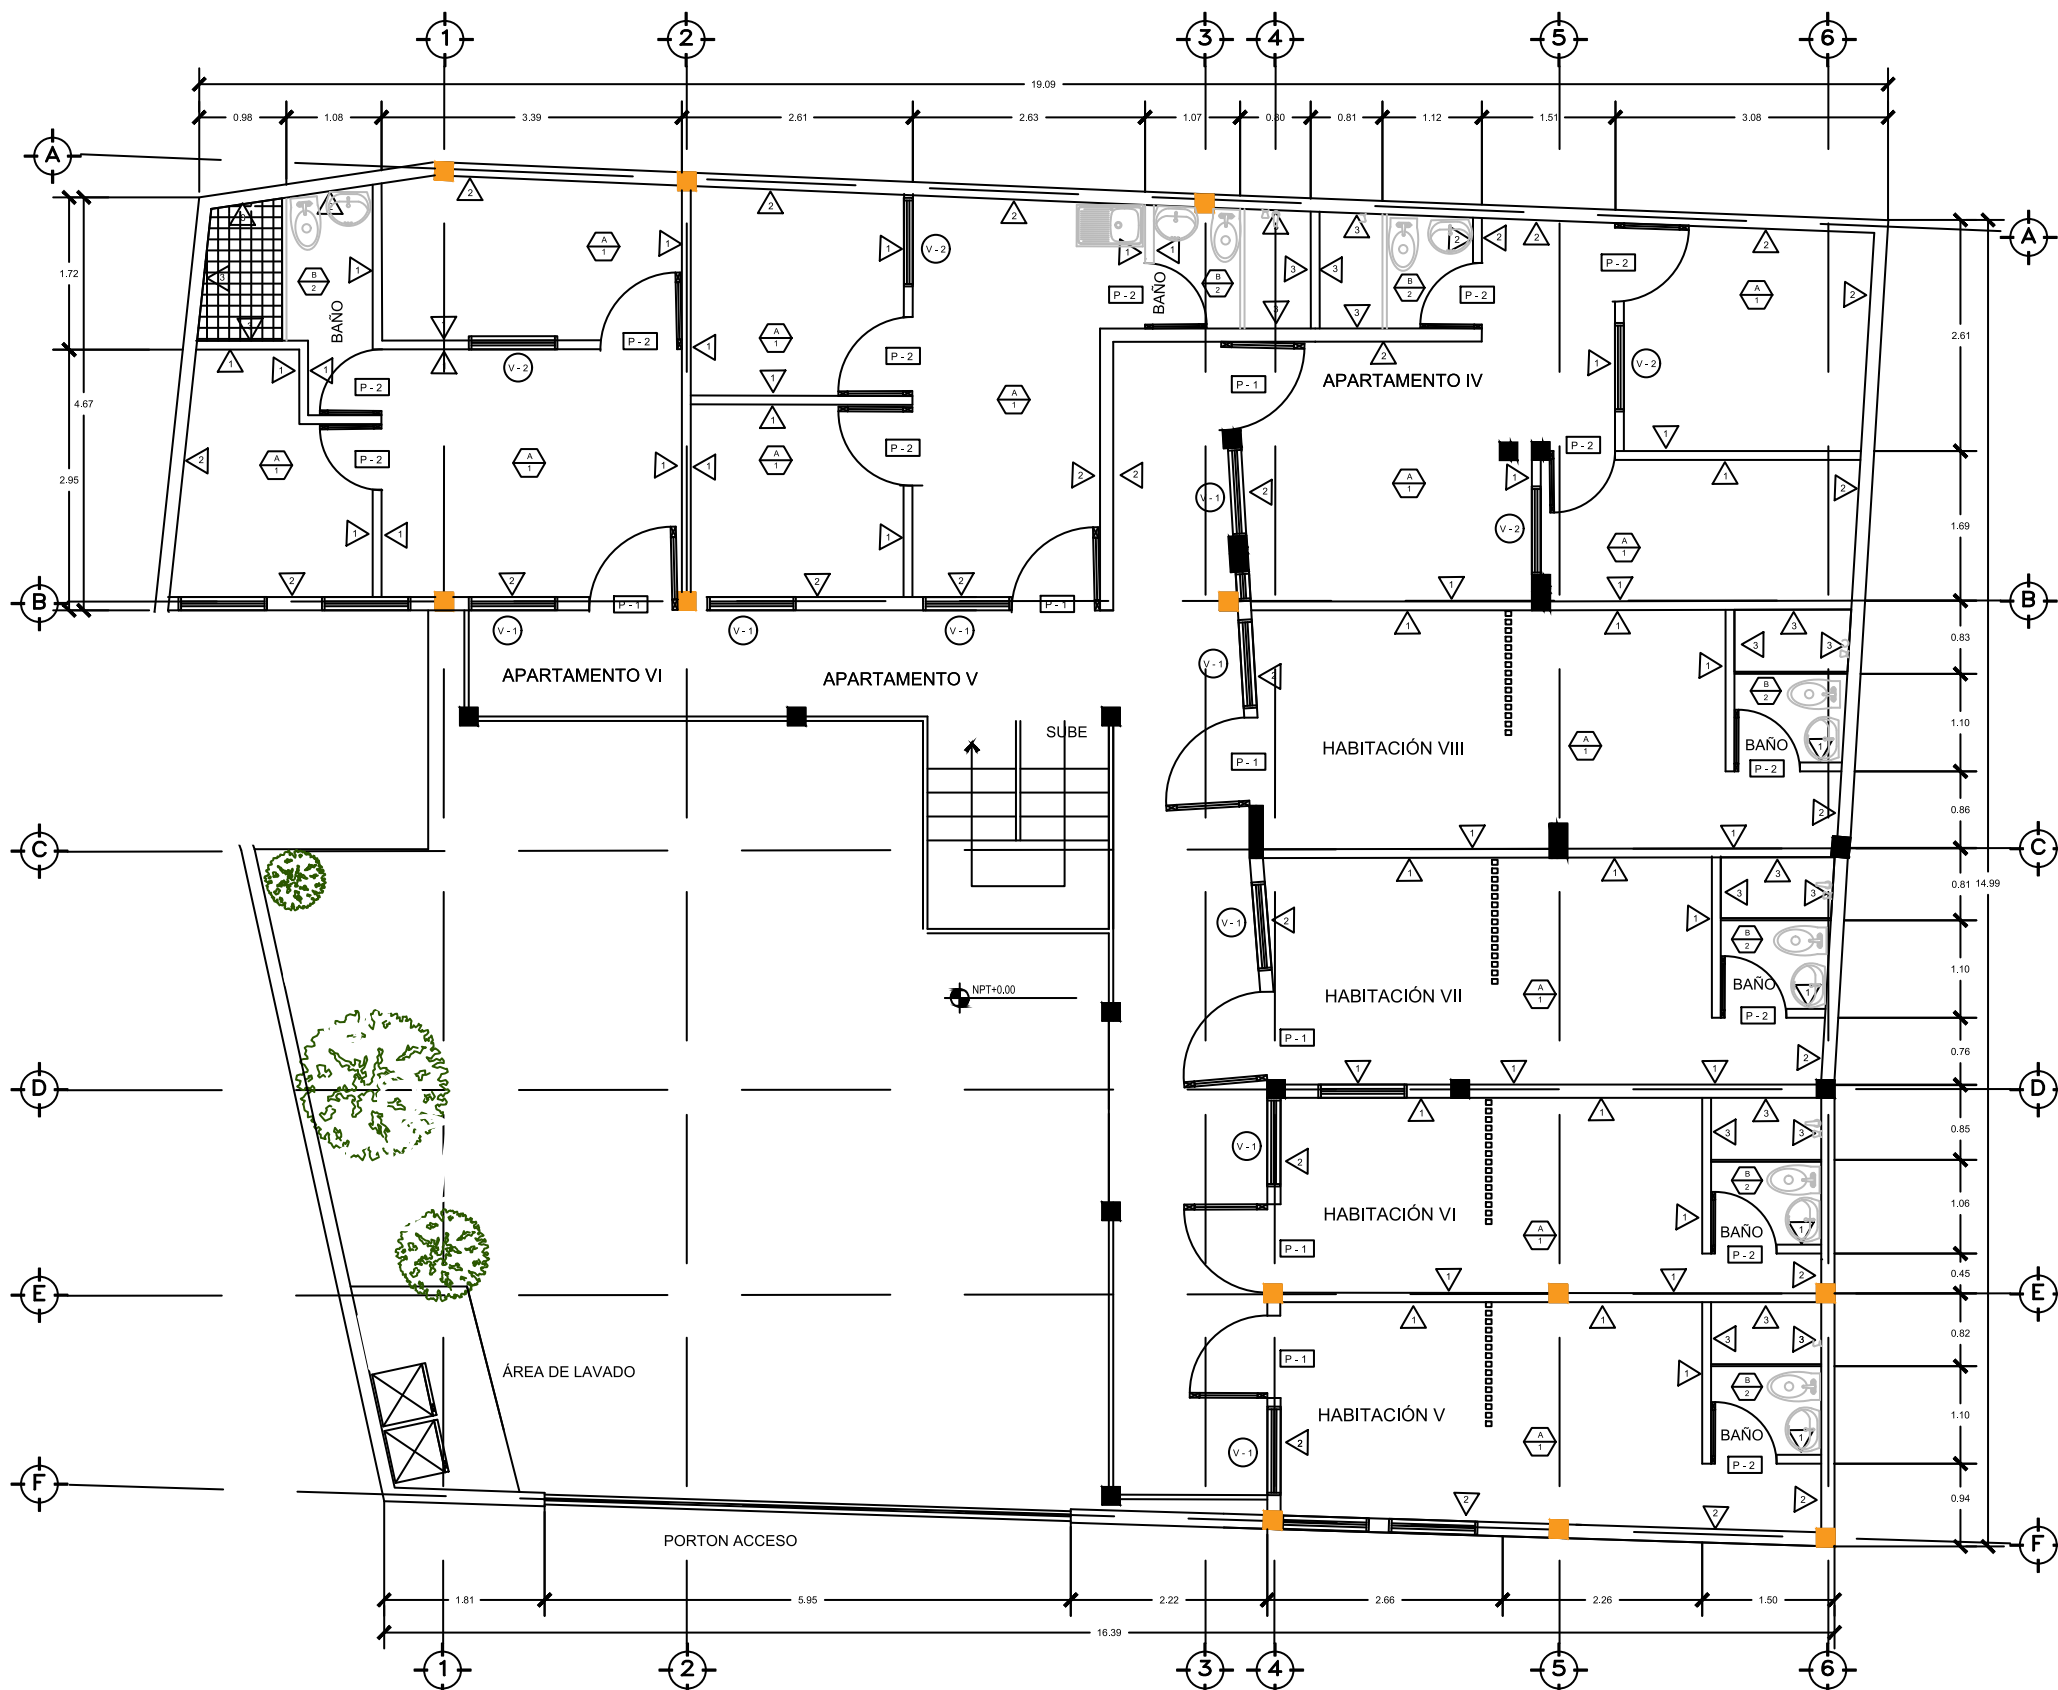

CUADRO DE PAREDES	
CLAVE	ESPECIFICACIONES TÉCNICAS
	PARED DE TABLA YESO, AFINADA, LIJADA Y PINTADA, COLOR GRIS SHERWIN WILLIAMS 7064
	PARED DE BLOQUE DE CONCRETO 20x40, REPELLADO, AFINADO PINTADO COLOR GRIS SHERWIN WILLIAMS 7066
	PARED DE TABLAYESO, AFINADA LIJADA Y PINTADA, CON BASE ACEITE COLOR BLANCO EXCELO LATEX, DENSIGLASS CON ENCHAPÉ DESDE NPT HASTA 1.80 MTS. PEZA DE CERAMICO BEIGE 20x30

CUADRO DE PUERTAS			
CLAVE	ANCHO	ALTO	DESCRIPCION
	1,00	2,00	PUERTA METALICA GALVANIZADA , PINTADO CON ESMALTE COLOR NEGRO.
	0,74	2,00	PUERTA DE MADERA SECA , SEIS TABLEROS, PINTADO COLOR BLANCO CON AFINADO FINAL DE BARNIZ MARINO BRILLANTE

CUADRO DE VENTANAS			
CLAVE	ANCHO	ALTO	DESCRIPCION
	1.00	1.80	VENTANAS PAREDES PERMETRALES, VENTANAS ESTILO FRANCESA, ANTIRREFLEJO EXTERIOR MARCO DE ALUMINIO 6mm
	1.00	1.20	VENTANAS PAREDES HABITACIONES : VENTANAS ESTILO FRANCESA, ANTIRREFLEJO EXTERIOR MARCO DE ALUMINIO 6mm VENTANAS ESTILO FRANCESA

CUADRO DE CIELOS	
CLAVE	ESPECIFICACIONES TÉCNICAS
	CIELO FALSO DE TABLAROCA AFINADO, LIJADO PINTADO COLOR BLANCO
	CIELO FALSO DE TABLAROCA DENSIGLASS AFINADO, LIJADO PINTADO COLOR BLANCO

CUADRO DE PISOS	
CLAVE	ESPECIFICACIONES TÉCNICAS
	PISO CERAMICO 30x30, COLOR BEIGE EN TODAS LAS HABITACIONES
	PISO CERAMICO 20x20cm antideslizante color blanco

PROYECTO:

REMODELACION CASA CALIFORNIA

CONTENIDO:

PLANO DE ACABADOS NIVEL 2

PROYECTÓ:

ARQ. EYLEEN HERNANDEZ

ESCALA:

1:2500


FECHA:

18/05/2024

HOJA:

A4/4

PLANTA ARQUITECTÓNICA NIVEL 2
ACABADOS
ESCALA 1:2500

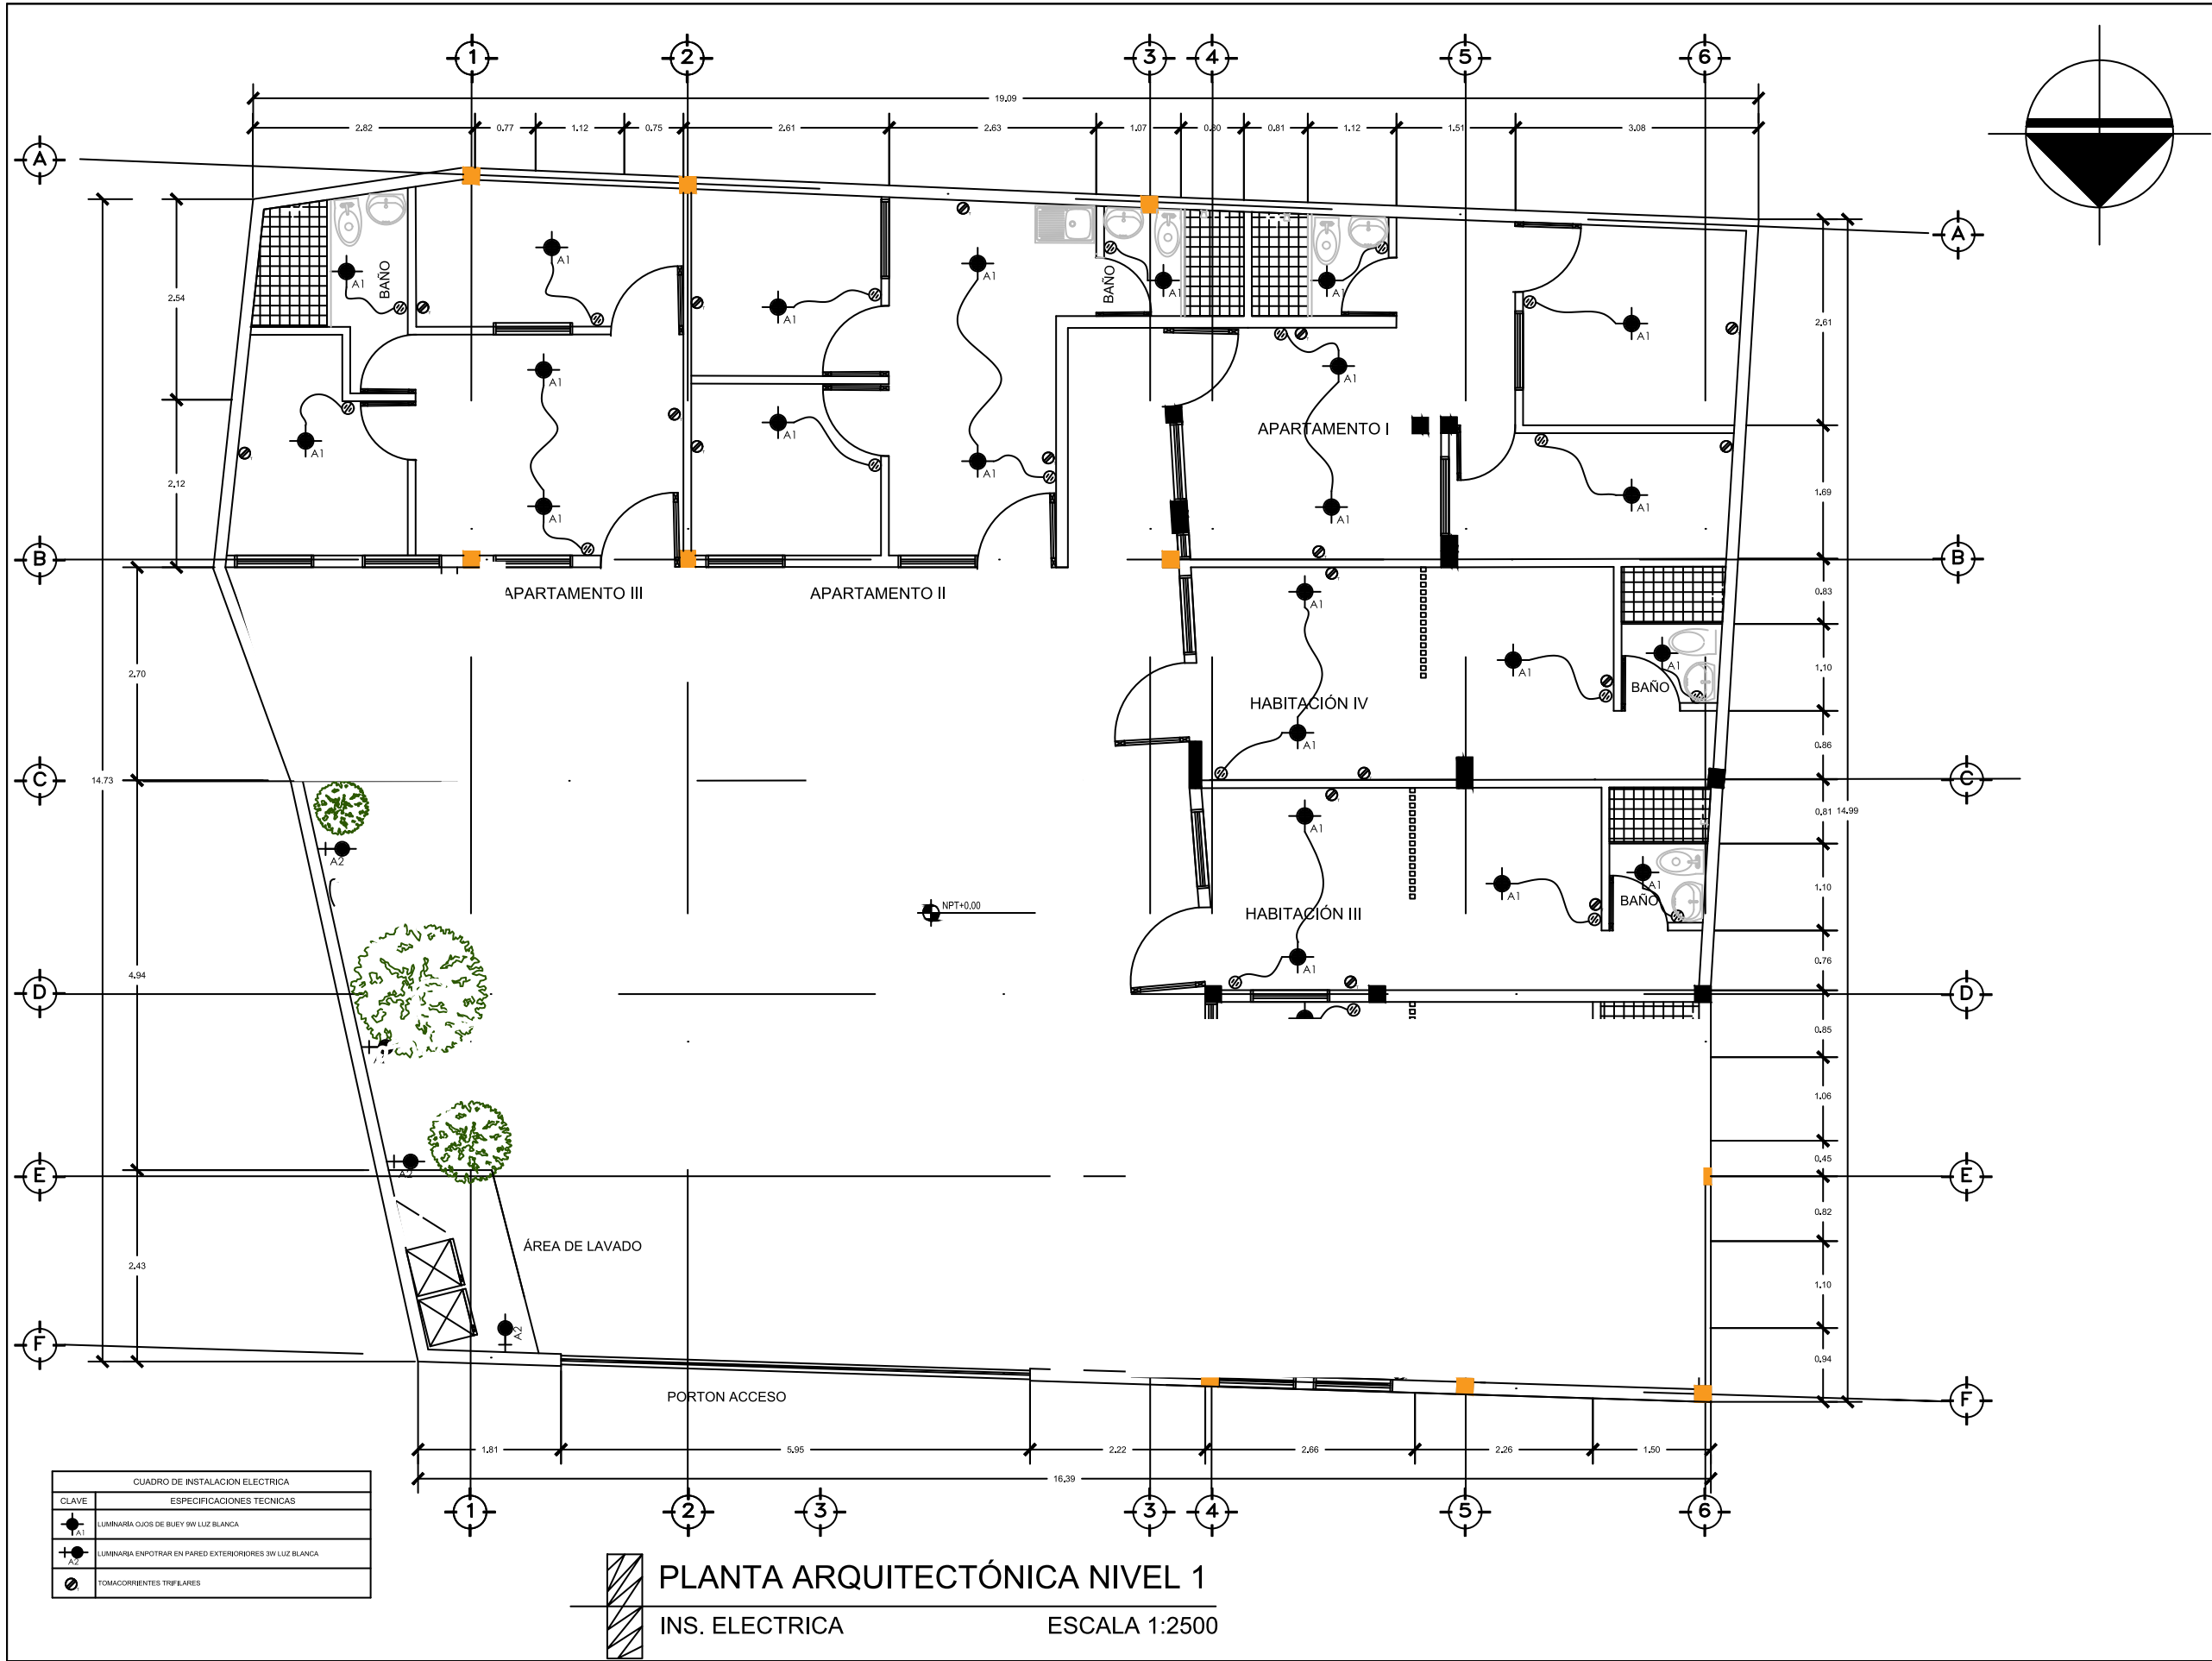

CUADRO DE INSTALACION ELECTRICA	
CLAVE	ESPECIFICACIONES TECNICAS
A1	LUMINARIA OJOS DE BUEY 9W LUZ BLANCA
A2	LUMINARIA EMPOTRAR EN PARED EXTERIORES 3W LUZ BLANCA
⊙	TOMACORRIENTES TRIFILARES



PLANTA ARQUITECTÓNICA NIVEL 1

INS. ELECTRICA

ESCALA 1:2500

PROYECTO:

REMODELACION CASA CALIFORNIA

CONTENIDO:

PLANO DE INSTALACION ELECTRICA NIVEL 1

PROYECTÓ:

ARQ. EYLEEN HERNANDEZ

ESCALA:


1:2500

FECHA:

18/05/2024

HOJA:

E1/2

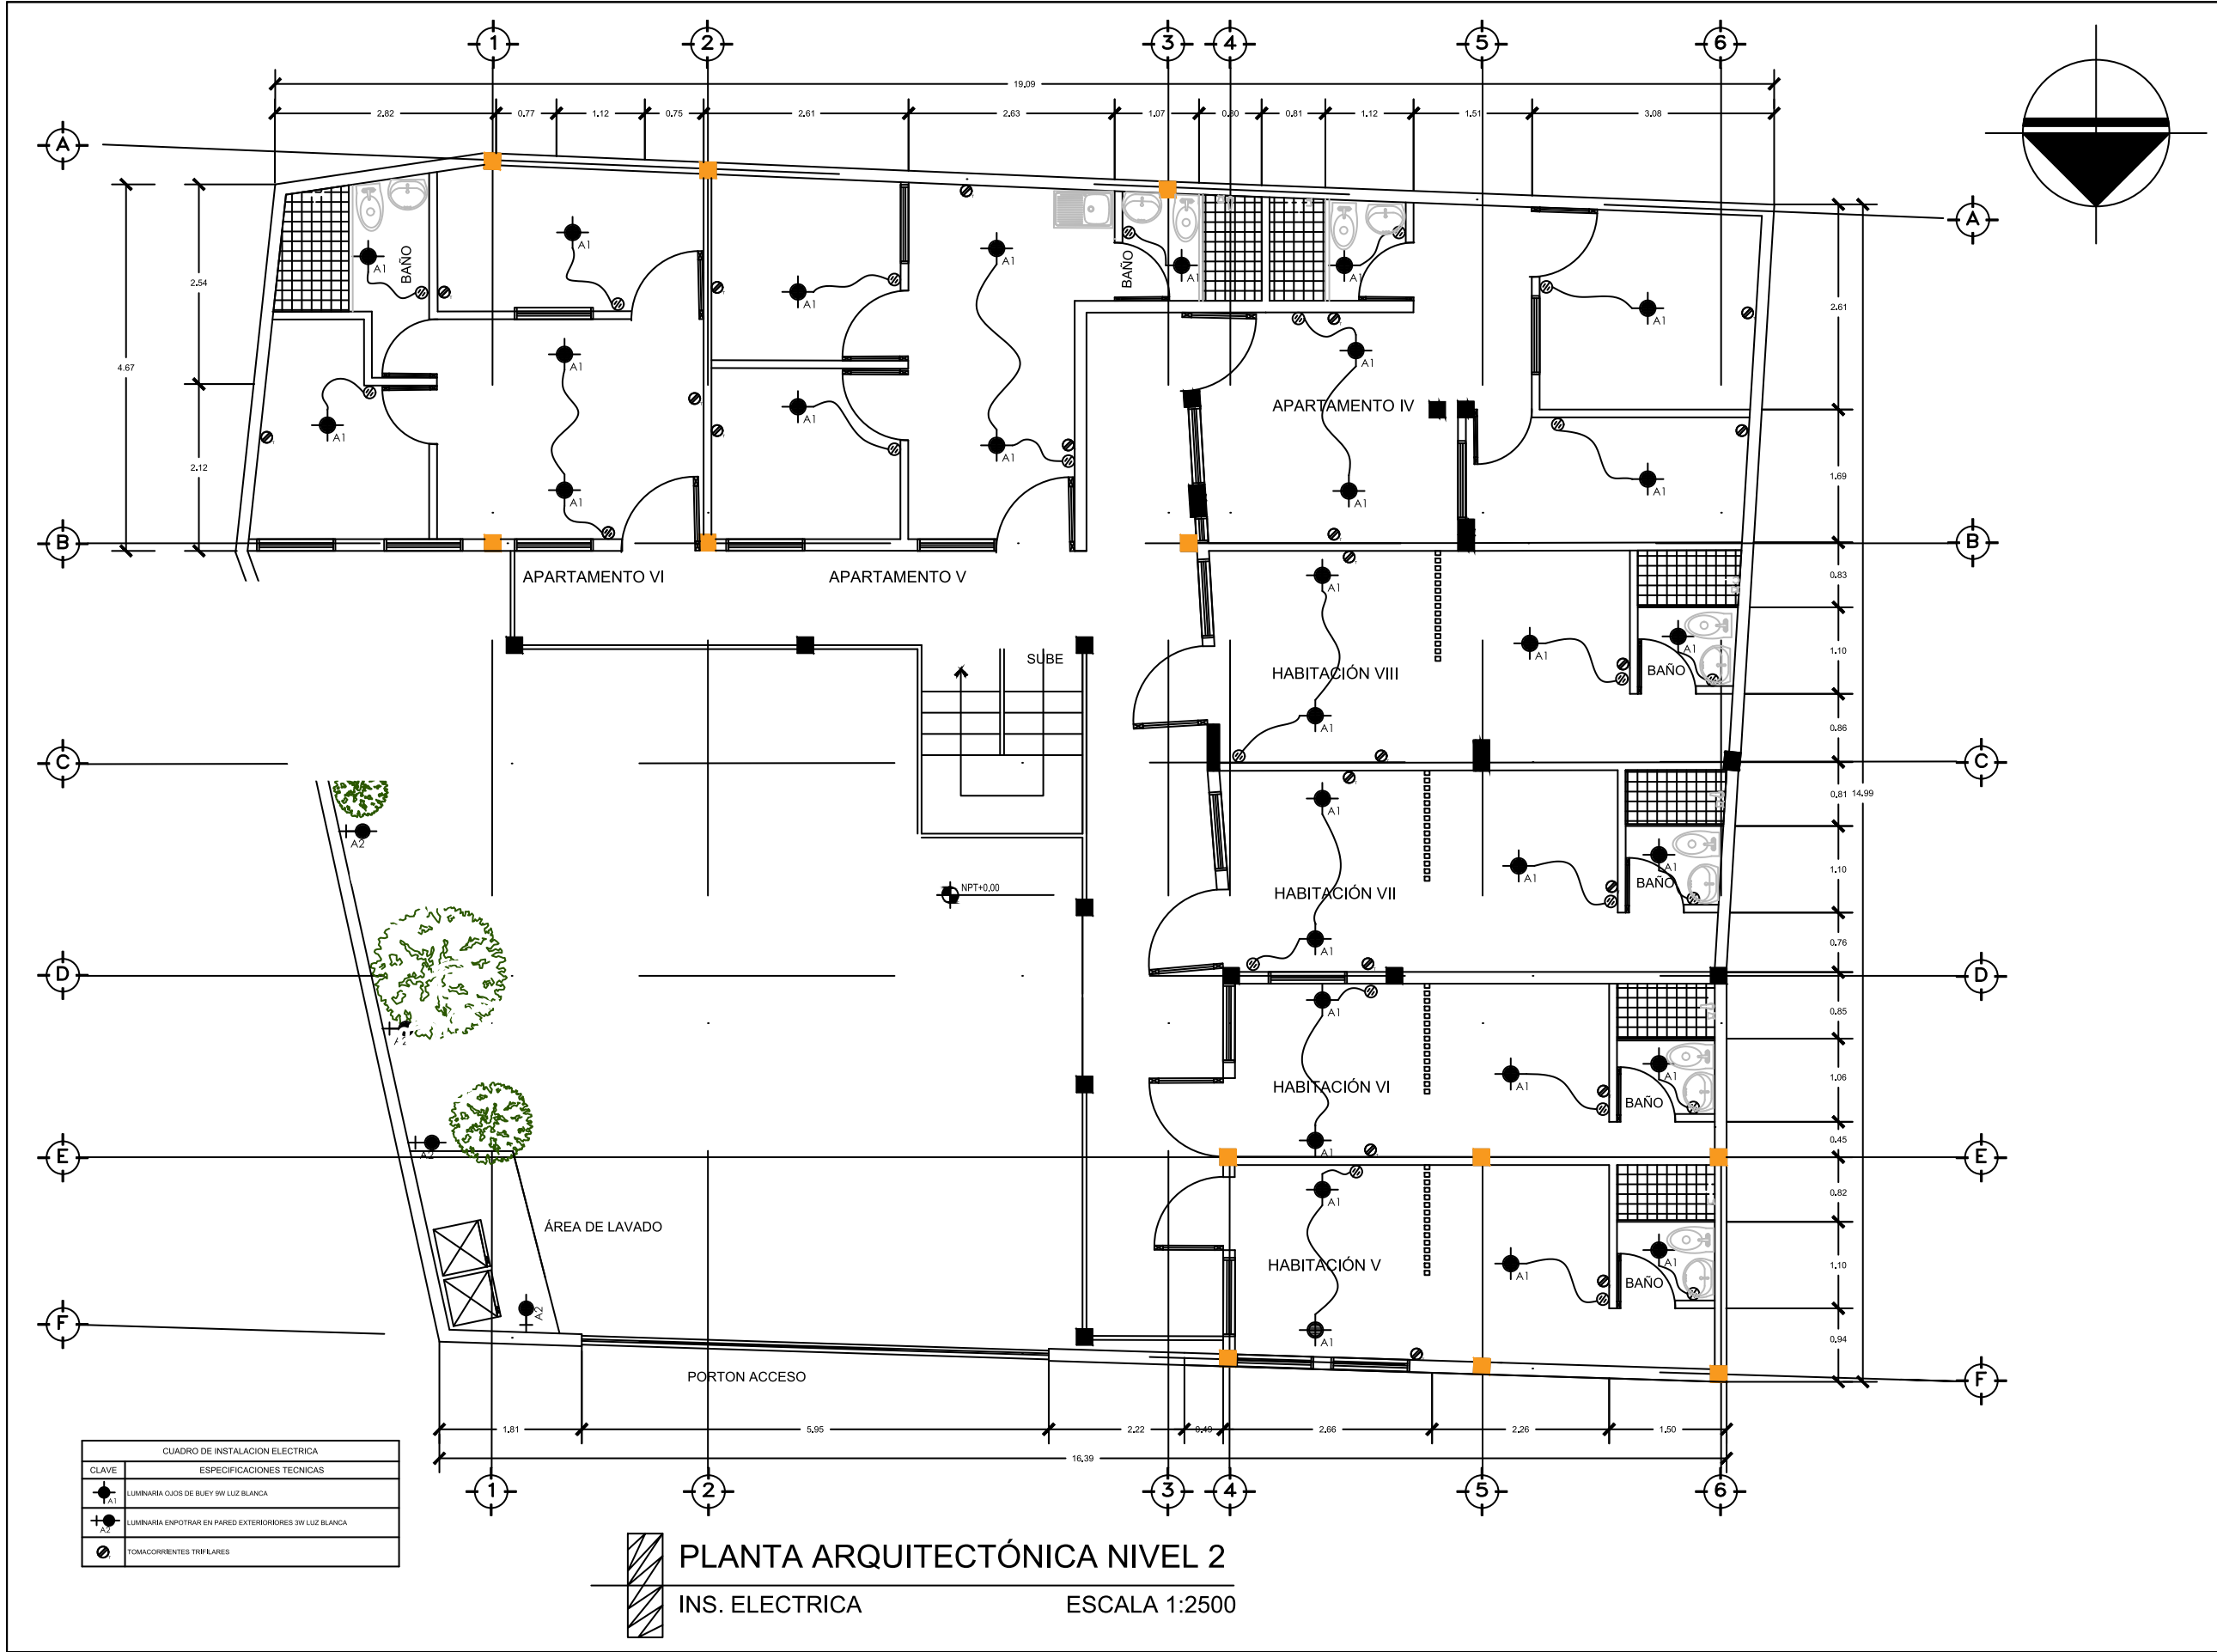

CUADRO DE INSTALACION ELECTRICA	
CLAVE	ESPECIFICACIONES TECNICAS
A1	LUMINARIA OJOS DE BUEY 9W LUZ BLANCA
A2	LUMINARIA EMPOTRAR EN PARED EXTERIORES 3W LUZ BLANCA
⊗	TOMACORRIENTES TRIFILARES



PLANTA ARQUITECTÓNICA NIVEL 2
INS. ELECTRICA
ESCALA 1:2500

PROYECTO:

REMODELACION CASA CALIFORNIA

CONTENIDO:

PLANO DE INSTALACION ELECTRICA NIVEL 2

PROYECTÓ:

ARQ. EYLEEN HERNANDEZ

ESCALA:


1:2500

FECHA:

18/05/2024

HOJA:

E2/2

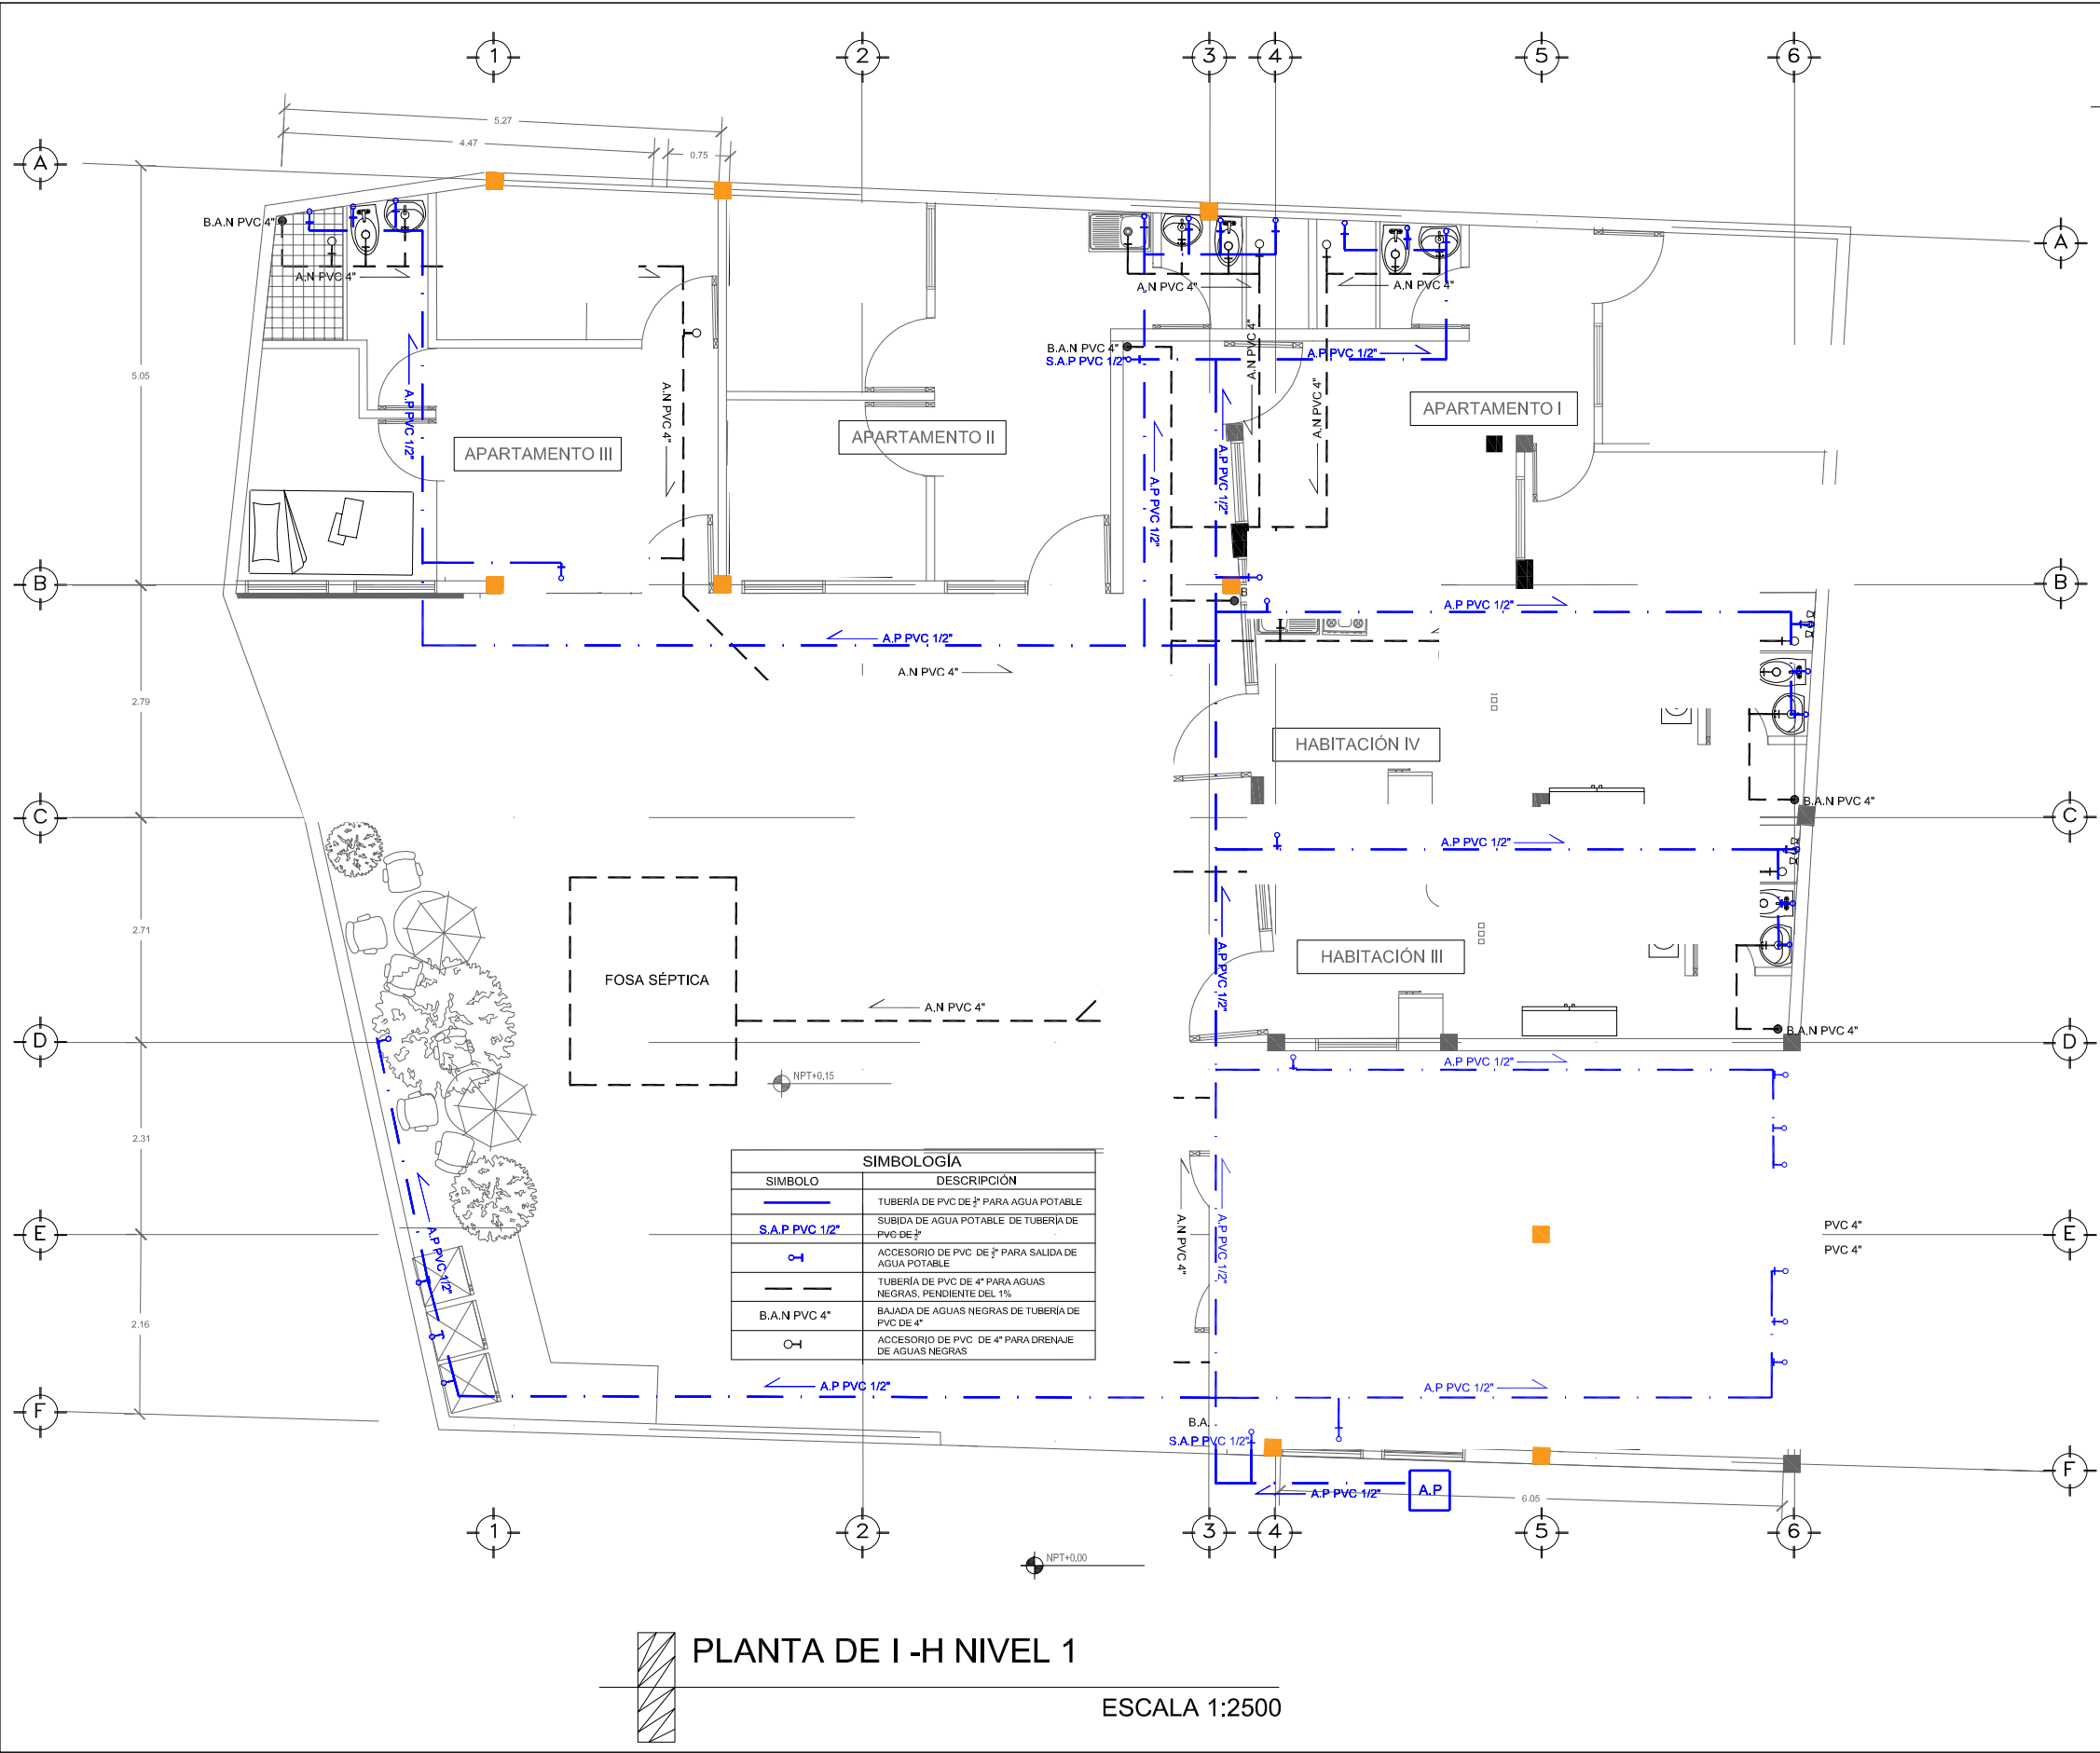

PROYECTO:

REMDELACION CASA CALIFORNIA

CONTENIDO:

PLANO DE INSTALACIONES HIDRÁULICAS-NIVEL 1

PROYECTÓ:

ARQ. EMILIA SALGUERO

ESCALA:


INDICADA

FECHA:

18-MAYO-2024

HOJA:

1/I-H

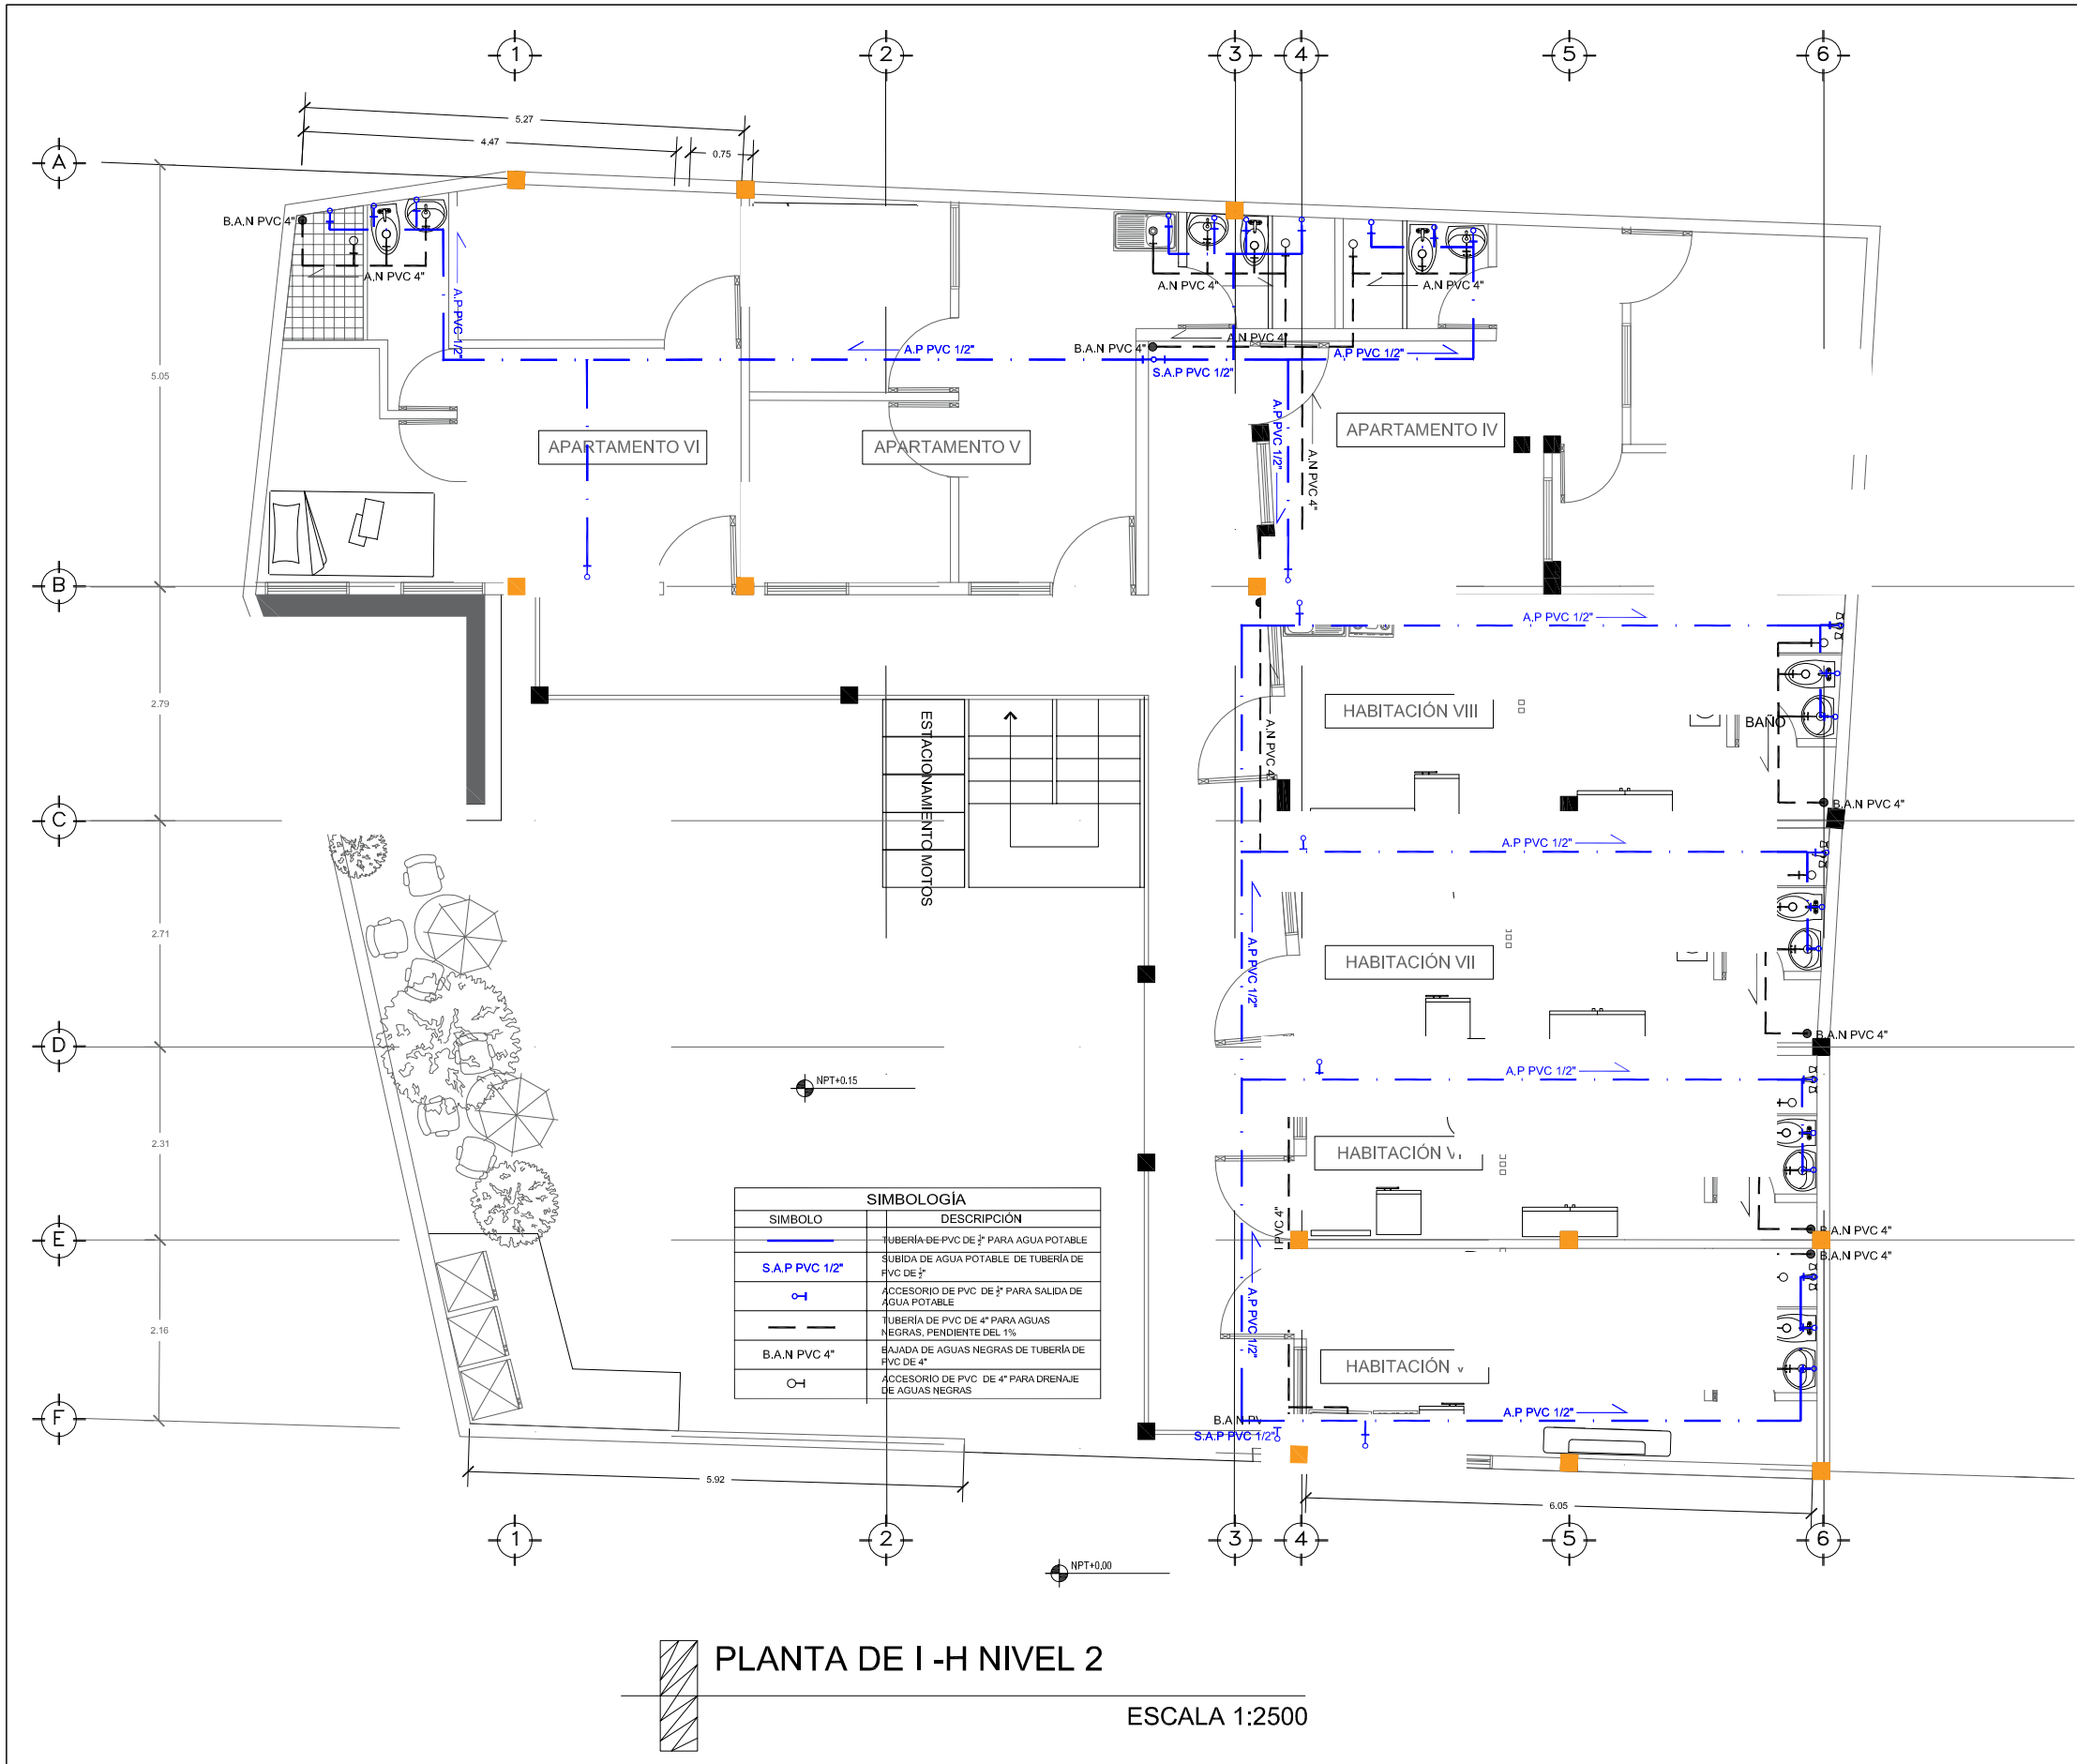

PLANTA DE I -H NIVEL 2

ESCALA 1:2500

PROYECTO:

REMODELACION CASA
CALIFORNIA

CONTENIDO:

PLANO DE INSTALACIONES
HIDRÁULICAS-NIVEL 2

PROYECTÓ:

ARQ. EMILIA SALGUERO

ESCALA:

INDICADA

FECHA:

18-MAYO-2024

HOJA:

2/I-H